


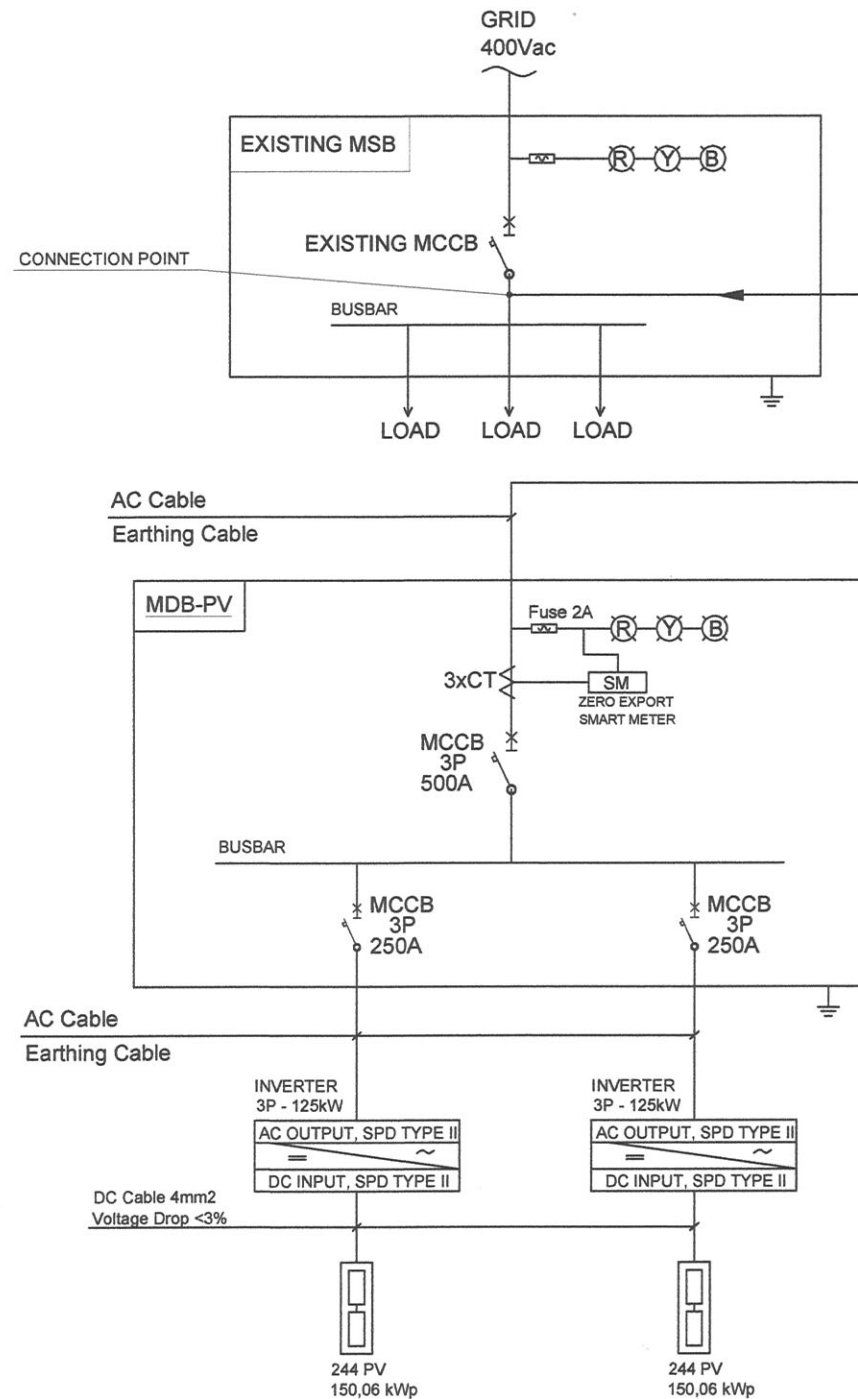

CÔNG TY TNHH STRIDE SOLAR

stride



Lê Hải Trà

MỤC ĐÍCH PHÁT HÀNH/ ISSUED FOR:

- ☐ TRÌNH DUYỆT/ FOR APPROVAL
- ☐ THAM KHẢO/ FOR REFERENCE
- ☒ THI CÔNG/ FOR CONSTRUCTION
- ☐ ĐẦU THẦU/ FOR TENDER
- ☐ HOÀN CÔNG/ AS-BUILT

TÊN DỰ ÁN/ PROJECT NAME:

CÔNG TY TNHH THƯƠNG MẠI SẢN XUẤT DỆT PHÚ AN

INVESTOR
PHU AN TEXTILE MANUFACTURING TRADING LIMITED COMPANY

46/15 Lê Đình Thám Street, Tân Quý Ward, Tân Phú District, Hồ Chí Minh City, Vietnam

NHÀ THẦU EPC/ EPC CONTRACTOR:
LIGHT SOLAR COMPANY LIMITED



105 Street No. 5, Lakeview City Area, An Phú Ward, Thủ Đức City, Hồ Chí Minh City, Vietnam

GIÁM ĐỐC/ DIRECTOR:

KIỂM TRA/ CHECKED:

THIẾT KẾ/ DESIGN:

TÊN BẢN VẼ/ DRAWING TITLE:

SINGLE LINE DIAGRAM
AC002641

TRANG/ NO. TỶ LỆ/ SCALE NGÀY/ DATE

1:1 .../10/202...

REV MÃ BẢN VẼ/ DRAWING CODE